


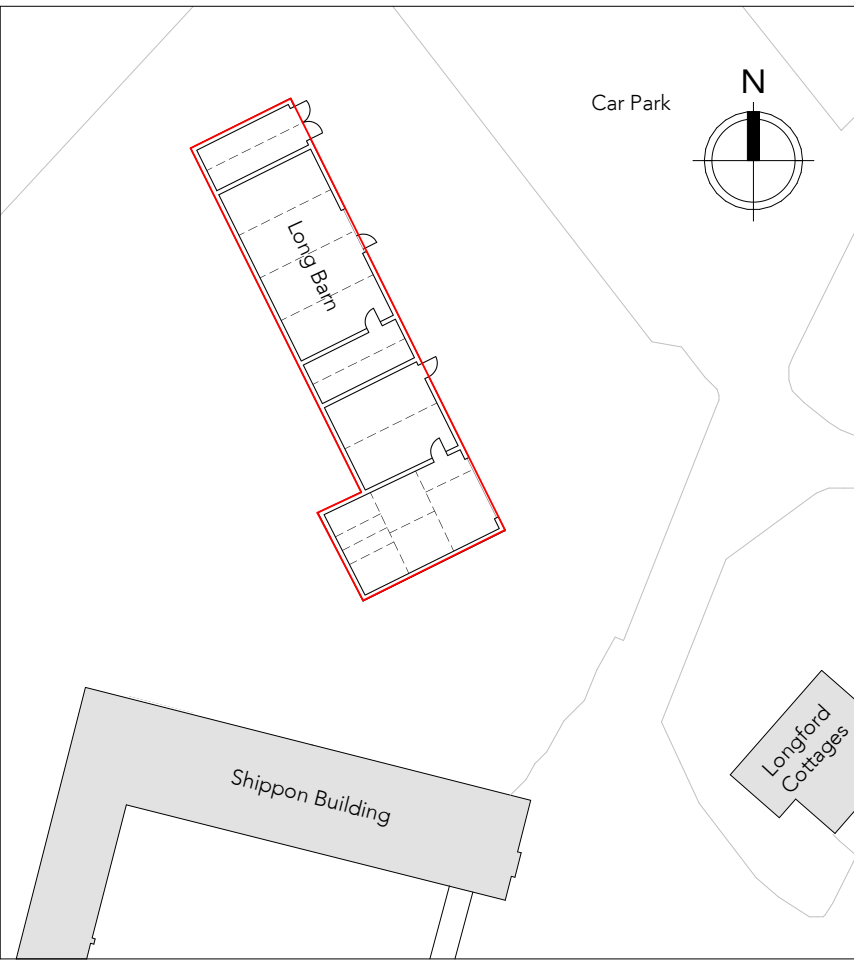

Note:
Do Not Scale from this drawing.
Dimensions are to be checked on site.
If in doubt please ask.



NOTE:
All construction shall be undertaken and completed in strict accordance with all drawings, specifications, statutory Building and Planning regulations, Health and Safety regulations, all relevant codes of practice requirements and manufacturers' recommendations and instructions.

Any discrepancies in constructional information should be reported immediately to the Architect/ contract administrator prior to commencement of any work.

Drawing are to be read in conjunction with any Specifications and Structural Engineer's details.

All dimensions must be checked on site before proceeding. Dimensions of new work are to be adjusted to suit the existing elevation where necessary. Do not assume that the existing structure or details are plumb, square or level. Drawings should not be scaled off.

For full package of Longford Park drawings for entire Masterplan scheme, see TEP information.

P01 30.09.22 TG PLANNING

Rev Date Intls Details

© The moral rights of the author are hereby asserted.
This drawing and design is the sole property of Buttress Ltd and must not be reproduced without permission.
Buttress Ltd is Registered in England and Wales: 5383573

Buttress

41 Bengal Street
Manchester
M4 6AF

T 0161 236 3303
E contact@buttress.net
W www.buttress.net

Project Title Longford Barn
Client Trafford Council
Location Stretford, Manchester

Drawing ref Proposed Ground GA


Date 10/10/2022 15:39:57 Scale As indicated

Checker AL Size A1

Job No: 9346 Status 50 Initial Status

Project Origin Volume Level Type Role Number Rev

LNGBN-BUT-ZZ-GF-DR-A-04001-P01

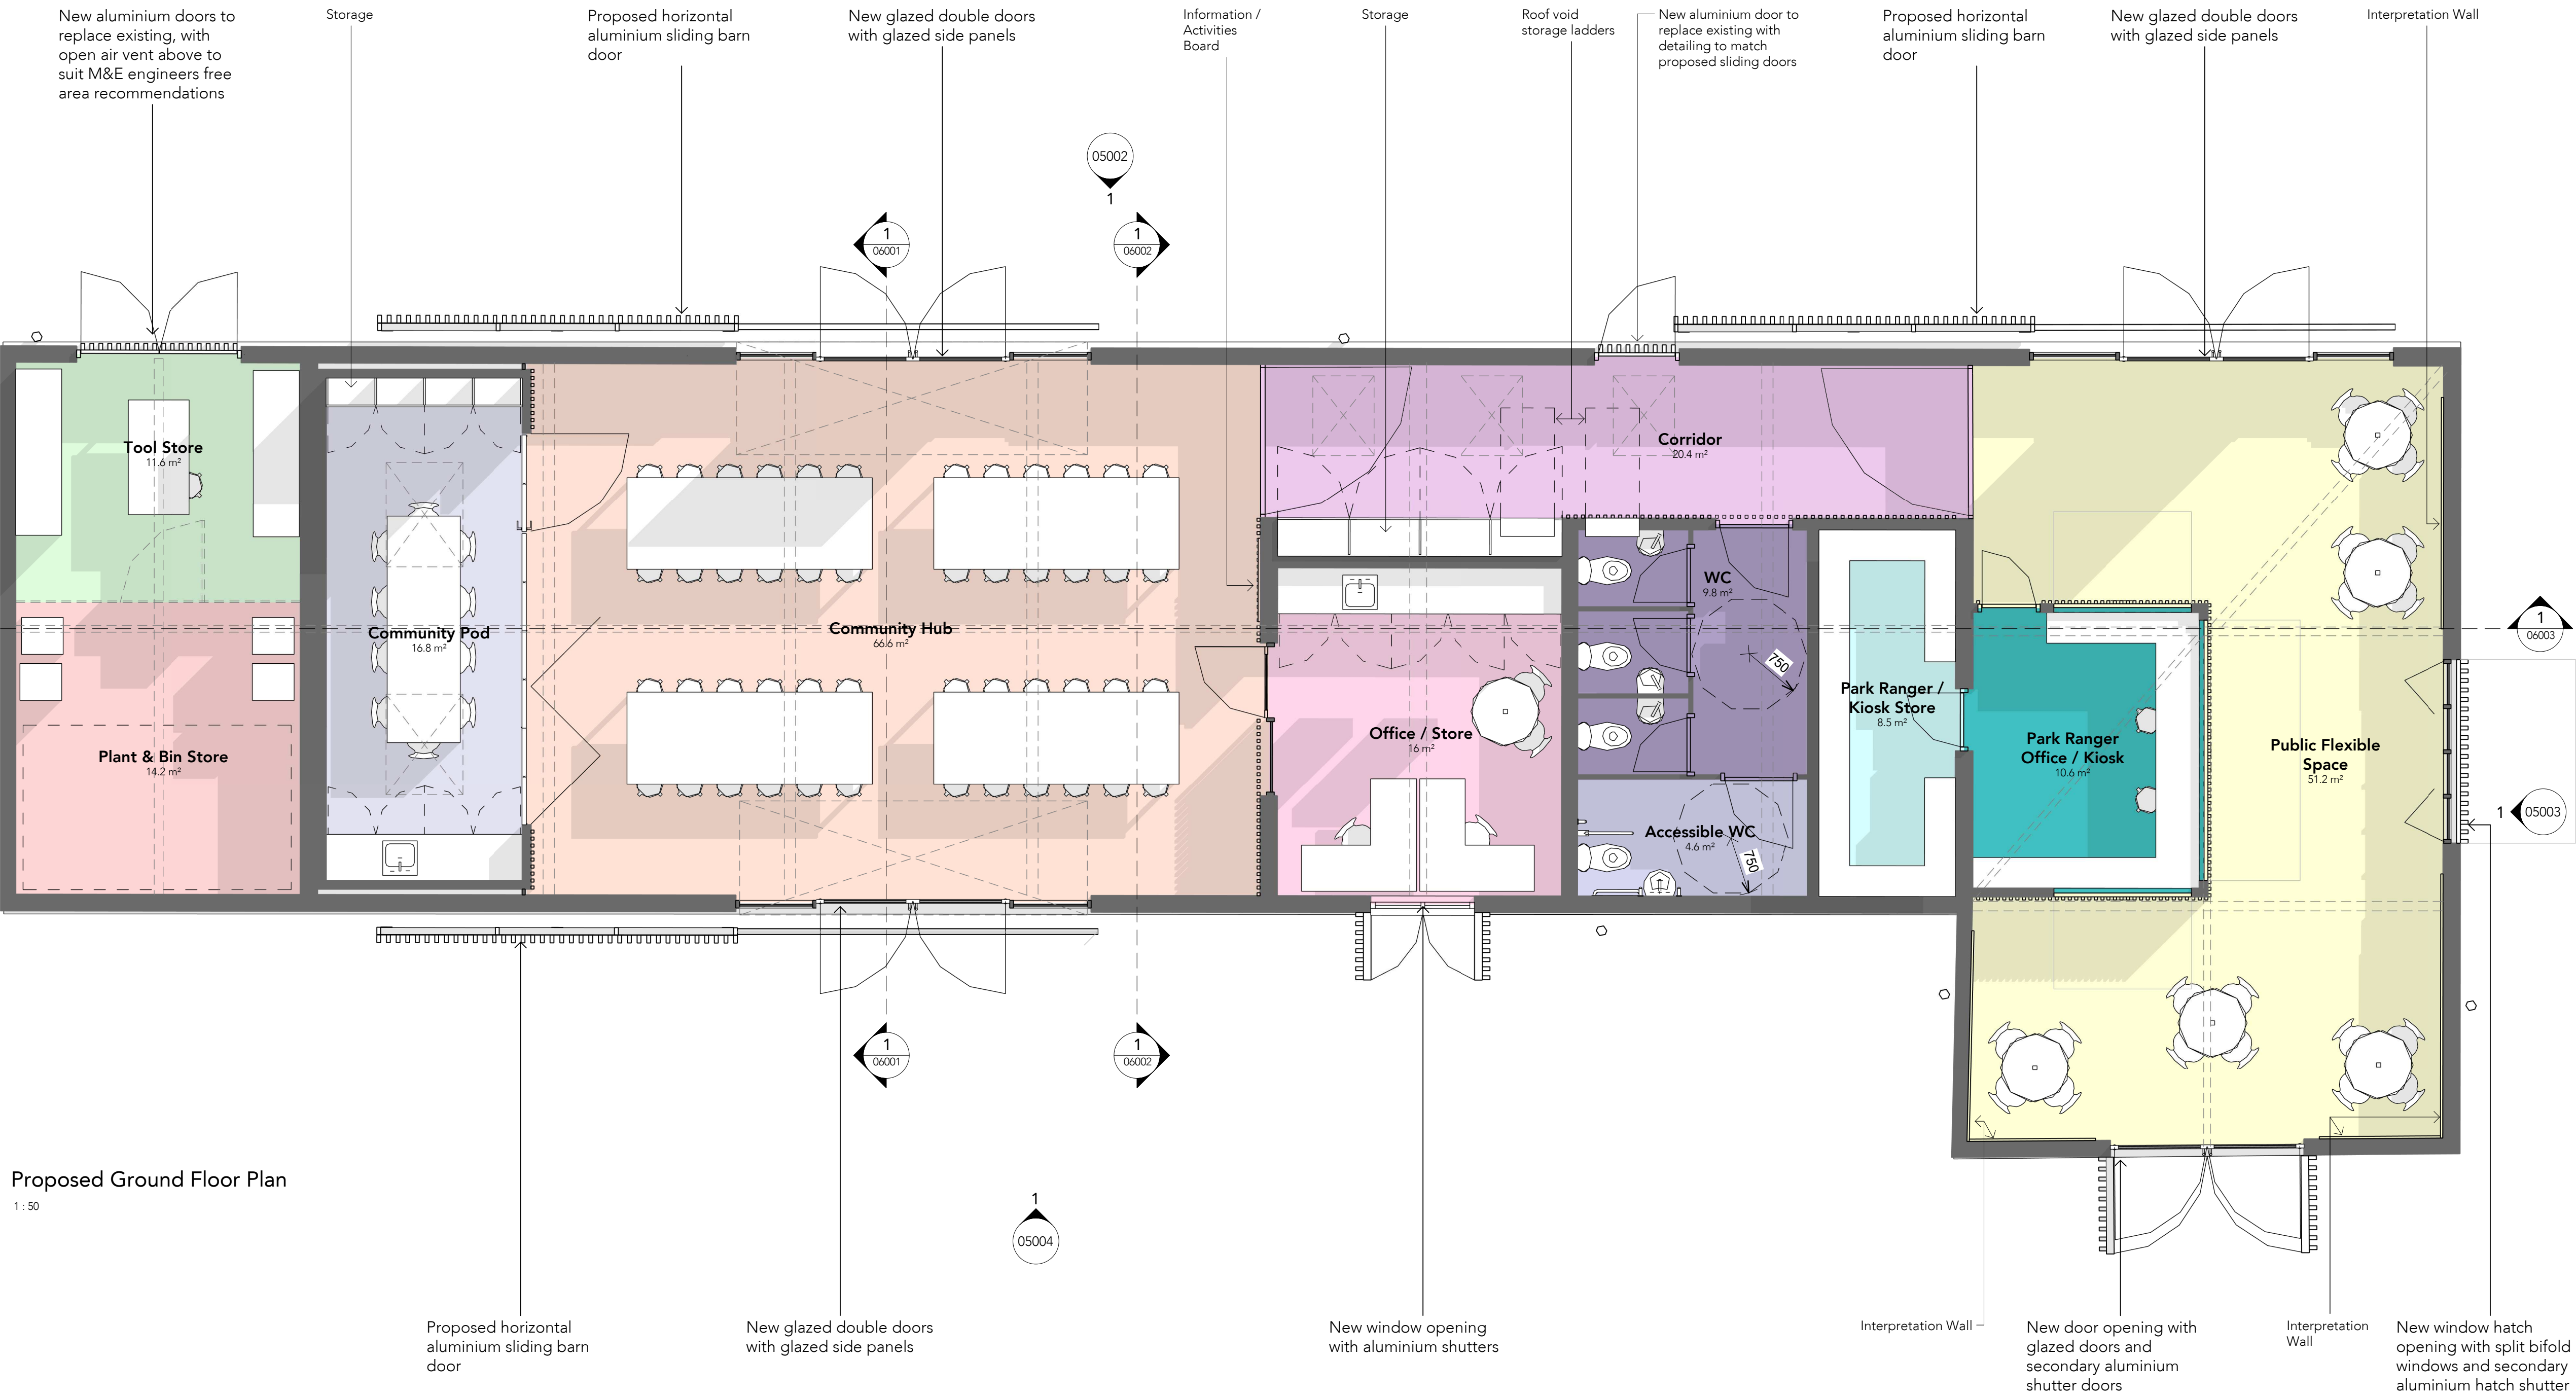

Proposed Ground Floor Plan
1 : 50

0.5 0 0.5 1 1.5 2 2.5 m
SCALE 1:50

